PLOT PLAN
LOT 39,
THE RIDGE AT CRYSTAL VALLEY RANCH FILING NO. 1,
TOWN OF CASTLE ROCK, COUNTY OF DOUGLAS,
STATE OF COLORADO

GENERAL NOTES:

THE ENTIRE PARCEL IS LOCATED WITH IN ZONE "X" AS SHOWN ON FIRM MAP NUMBER 08035C0303G, REVISED MARCH 16, 2016.

ANY ADJUSTMENTS WHICH MUST BE MADE TO UTILITY POLES, STREET LIGHT STANDARDS, FIRE HYDRANTS, CATCH BASINS OR INLETS, TRAFFIC SIGNS AND SIGNALS, OR OTHER PUBLIC IMPROVEMENTS OR INSTALLATIONS WHICH ARE NECESSARY AS THE RESULT OF THE CURB OPENINGS OR DRIVEWAYS SHALL BE ACCOMPLISHED WITHOUT ANY COST TO THE TOWN. DRIVEWAYS SHALL NOT INTERFERE WITH OPERATIONS OR LOCATIONS OF ANY DRAINAGE APPURTENANCES OR ADA RAMPS.


THIS PLAN IS IN CONFORMANCE WITH THE MINIMUM REQUIREMENTS AS SET FORTH IN THE RIDGE AT CRYSTAL VALLEY FILING NO. 1 SUBDIVISION GRADING PLAN AS APPROVED BY THE TOWN OF CASTLE ROCK ON 03/18/2022 UNDER APPROVAL NO. CD21-0016.

THIS LOT IS COVERED UNDER STANDARD TESC PERMIT NO. TESV23-0005.

NOTES:
ALL STRUCTURAL BMPS ASSOCIATED WITH THE CONSTRUCTION OF THE SPECIFIC LOT MUST BE MAINTAINED IN EFFECTIVE OPERATING CONDITION AT ALL TIMES AND ARE SUBJECT TO INSPECTION AND ENFORCEMENT UNDER THE BUILDING PERMIT FOR THIS PROPERTY.

MAXIMUM PERMITTED HEIGHT OF 35-FEET FOR LOTS LOCATED WITHIN THE MODERATE SKYLINE AREA (LOTS 1-13 AND LOTS 79-90) APPROVED BY THE PLANNING COMMISSION VIA SKY21-0001

BMP INSTALLATION STANDARD NOTES AND DETAILS ARE AVAILABLE AT CRGOV.COM/TESC

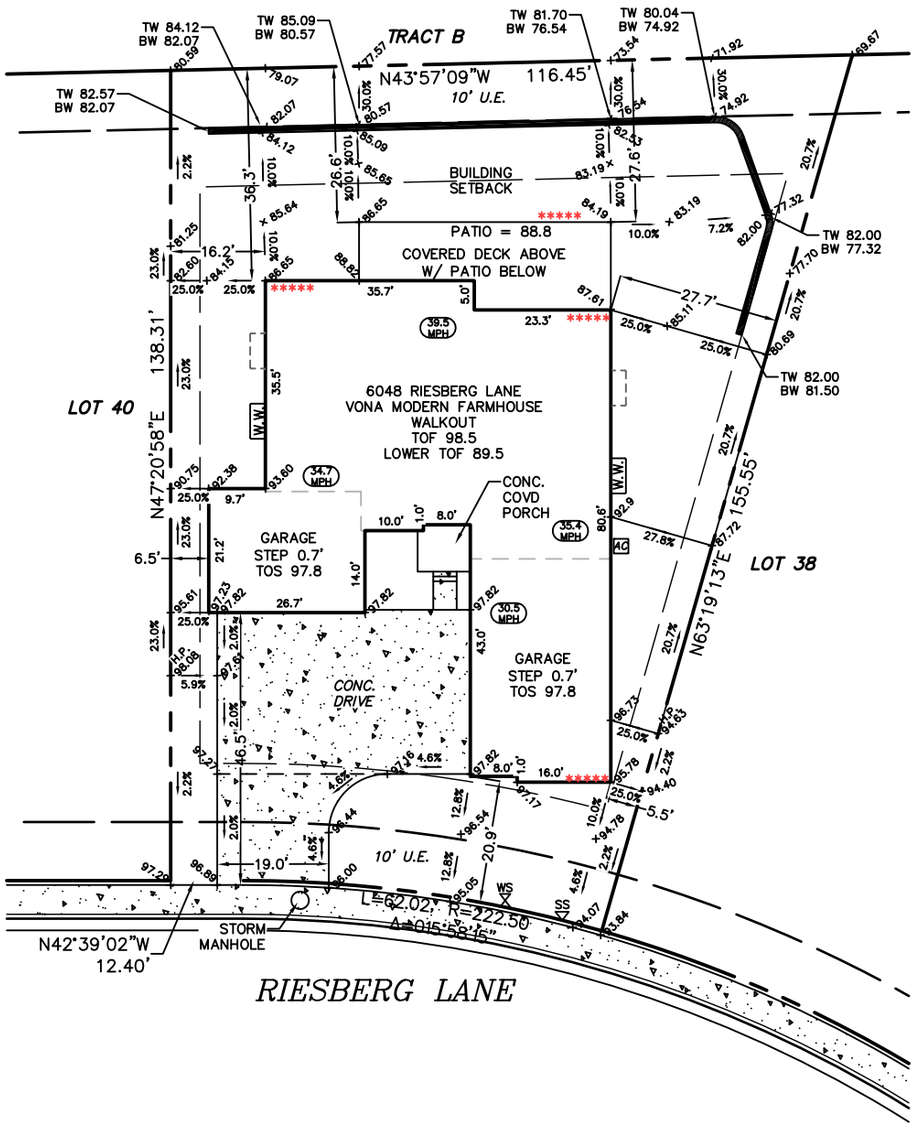

SCALE: 1" = 30'

SETBACKS:
FRONT: 20'
REAR: 20'
SIDE: 5'
CORNER: 10'

STRUCTURAL OPTIONS:
PC017 - WALKOUT BASEMENT
PC036026 - OPEN STAIRS TO LOWER LEVEL
PC263285 - ALTERNATE PRIMARY SHOWER
PC263428 - 5-CAR FRONT ENTRY GARAGE
PC263461 - ADDITIONAL ENTRY
PC812 - BUTLER PANTRY
PC026373 - MULTI SLIDE STACKED DOOR - 16X8
PC026789 - MULTI SLIDE STACKED DOOR - 16X8
PC543 - DAYLIGHT WINDOW/WELL
PC189202 - ALTERNATE COVERED DECK
PC189183 - EXPANDED REAR PATIO AT WALKOUT

NOTE: 2/20/2025 JLA ADJUST RETAINING WALL

FINAL GRADING MAY VARY DUE TO EXISTING SITE CONDITIONS

NOTICE: ACCORDING TO COLORADO LAW YOU MUST COMMENCE ANY LEGAL ACTION BASED UPON ANY DEFECT IN THIS SURVEY WITHIN THREE YEARS AFTER YOU FIRST DISCOVER SUCH DEFECT. IN NO EVENT, MAY ANY ACTION BASED UPON ANY DEFECT IN THIS SURVEY BE COMMENCED MORE THAN TEN YEARS AFTER THE DATE OF THE CERTIFICATION SHOWN HEREON

——>—— · · · —————— SWALE

(XX MPH) MPH IS MID POINT HOUSE

***** DEEPEN FOOTER FOR FROST PROTECTION

++++ STEP SIDING TO ACCOMMODATE GRADE

NOTE:
NUMBER OF RISERS IS APPROXIMATE:
MIN. OR AT LEAST 2 RISERS FROM DRIVEWAY TO FRONT PORCH
MIN. OR AT LEAST 3 RISERS FROM FINISHED FLOOR TO GARAGE SLAB

811 Know what's below. Call before you dig.

SITE DATA CHART

LOT SIZE	13,504 SQ FEET±
AVERAGE HEIGHT HOUSE	35.0 FEET±

ESE CONSULTANTS
ENGINEERING • PLANNING • SURVEYING • ENVIRONMENTAL
ESE Consultants, Inc.
7100 E. Belview Avenue, Greenwood Village, CO 80111
T: 720-677-9148

RIDGE AT CRYSTAL VALLEY, FILING NO. 1
TOWN OF CASTLE ROCK, COUNTY OF DOUGLAS, STATE OF COLORADO

TOLL#039
6048 RIESBERG LANE

DRAWN:	CHECKED:	DATE:	SCALE:	ORDER NUMBER:	FILE NAME:	SHEET NO.:
TS	JA	03.05.2024	1"=20'	BP081380039002	8138-L0039-PP-VONA-ADJUSTED	1 OF 1